

FX Bio 2공장 2층 설비 배치도 (가상)

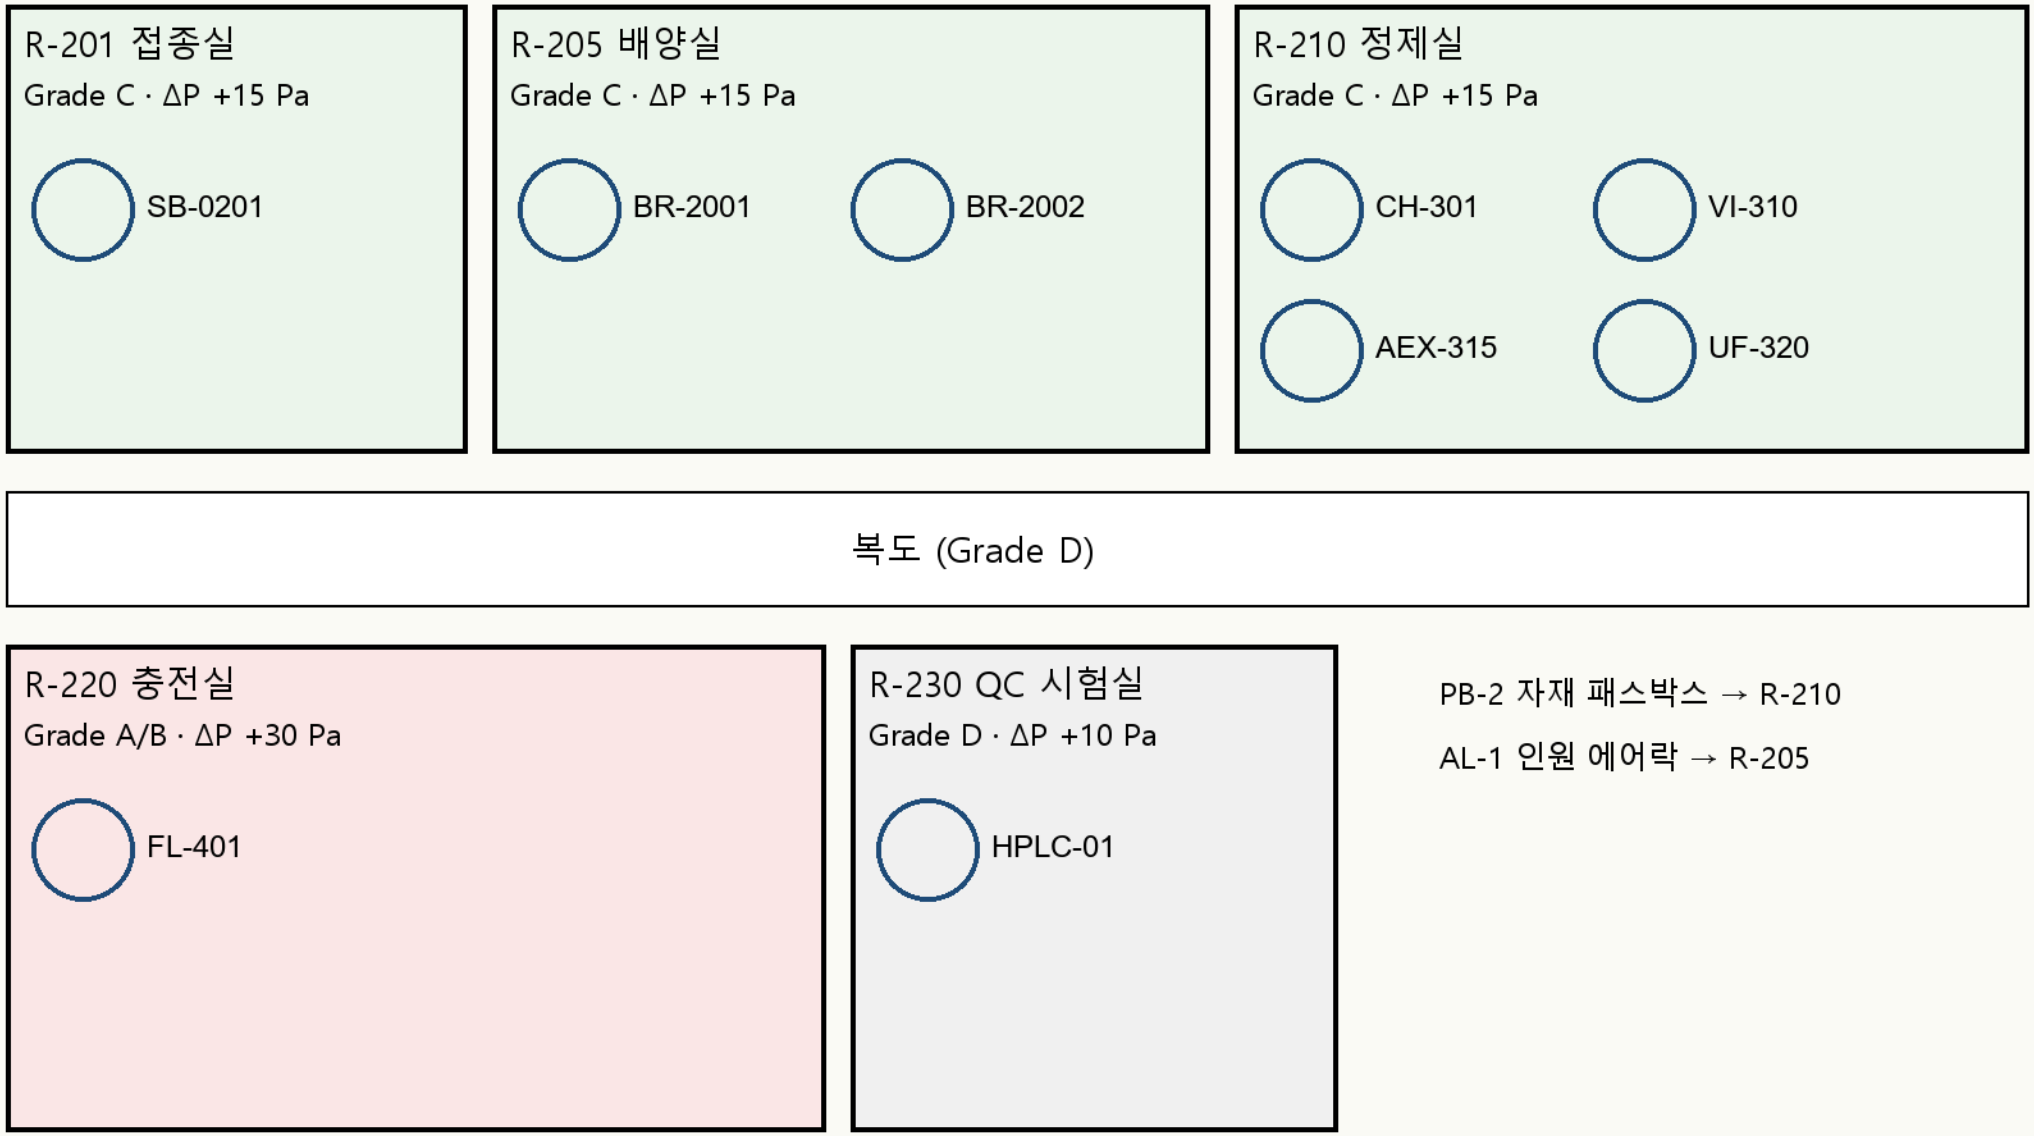

설비 목록 (스캔, 가상)

설비		위치·규격		현황
ID	설비	방	용량	상태
SB-0201	시드 배양기	R-201	200 L	가동
BR-2001	생물반응기(STR)	R-205	2,000 L	가동
BR-2002	생물반응기(STR)	R-205	2,000 L	점검
CH-301	Protein A 크로마토그래피	R-210	60 cm ID	가동
VI-310	바이러스 불활화 탱크	R-210	1,500 L	가동
AEX-315	음이온 교환 막	R-210	5 m²	가동
UF-320	UF/DF 스키드	R-210	25 m²	가동
FL-401	바이알 충전기	R-220	6,000 vial/h	가동

인원·자재 동선 (가상)

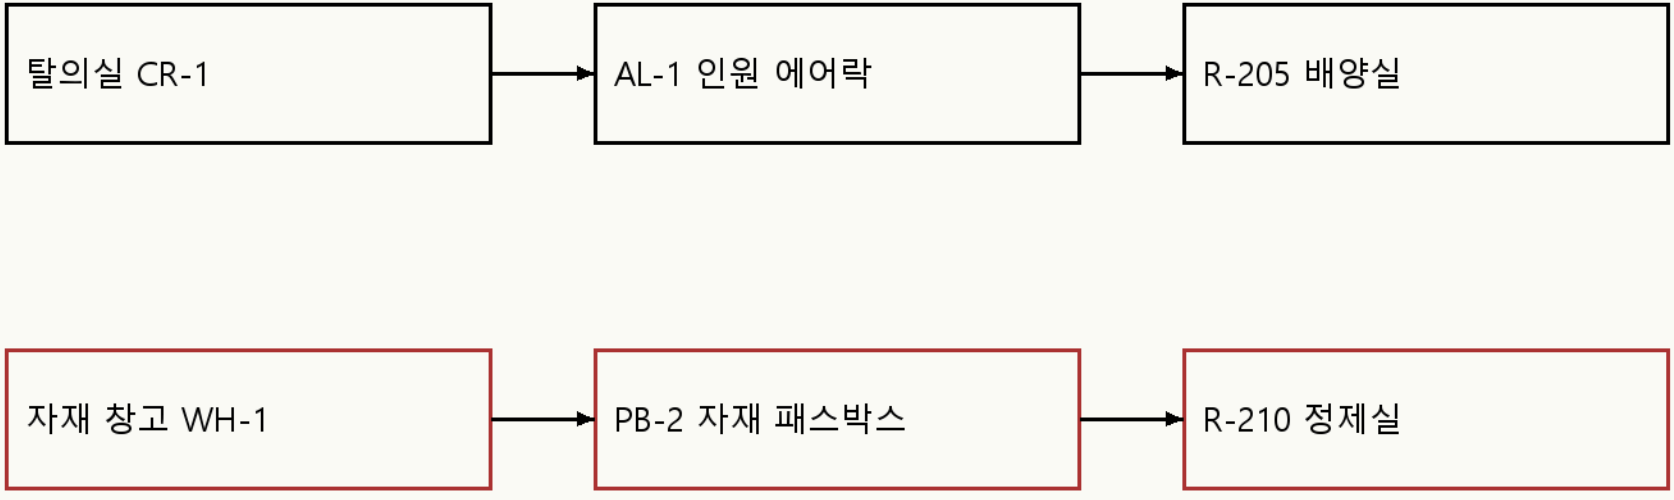

인원 동선: 검정 · 자재 동선: 빨강 · 교차 금지